


COLOURBOND ROOF
25° PITCH 450 EAVES

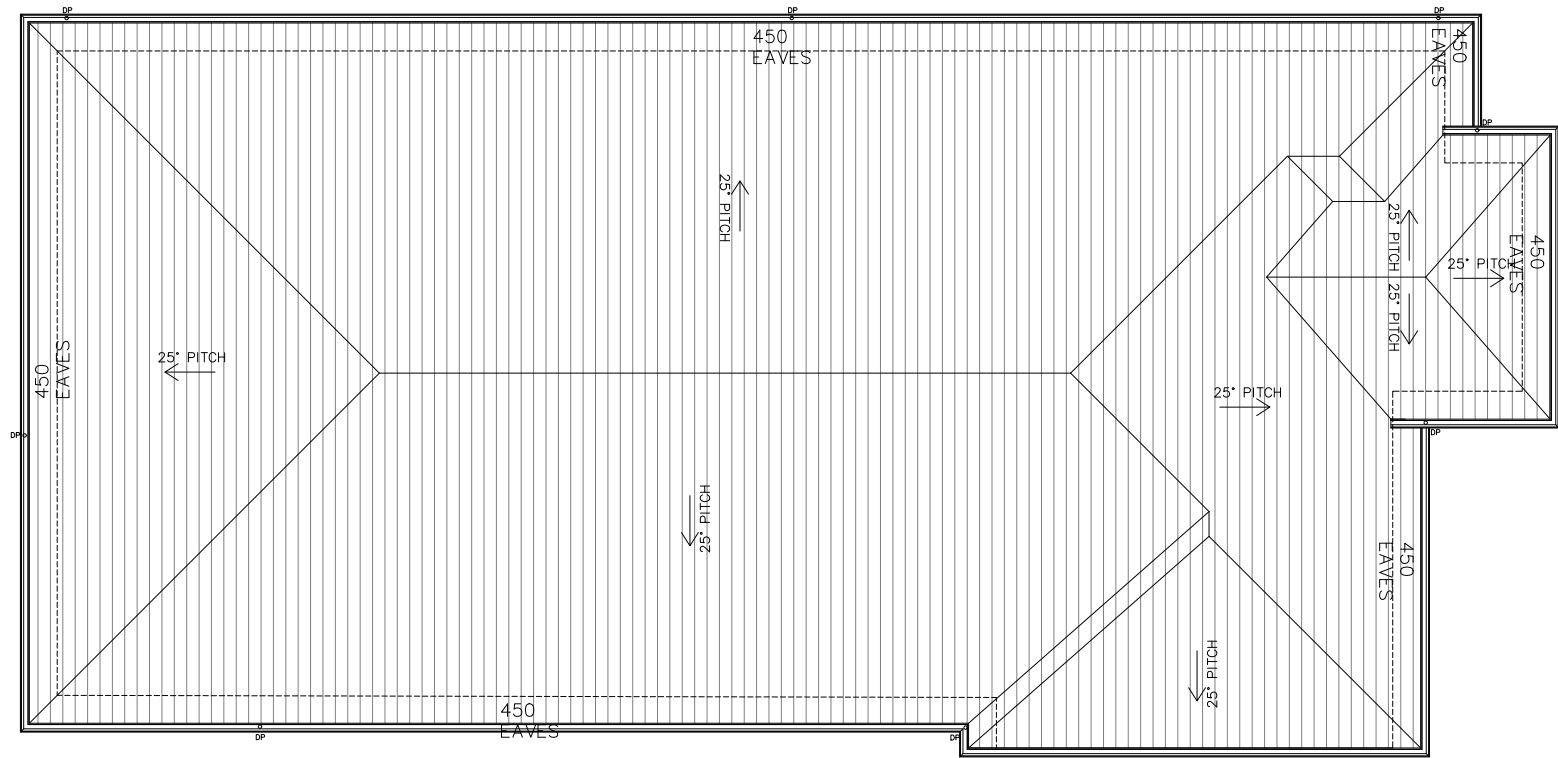

NOTES:

COLORBOND ROOF SHEET @ 25°
WITH COLORBOND FASCIA & GUTTER.

PVC PAINTED DOWNPIPES AS PER
BUILDERS SPEC.

COLORBOND METAL CAPPING BETWEEN
TWO WALL JUNCTIONS.

COLORBOND ROOF SHEETING TO
COMPLY WITH AS/NZ 2728:2013.

COLORBOND GUTTERS & DOWNPIPES
TO COMPLY WITH PART 3.5.3 OF BCA.


ROOF TRUSS AND WALL FRAMES TO
MANUFACTURER'S SPECIFICATIONS.

EXPANSION JOINTS ARE TO BE
PROVIDED IN ACCORDANCE
WITH ENGINEER'S SPECIFICATIONS.

EAVES OVERHANG AND GABLE ARE
MEASURED FROM INNER FACE OF
FASCIA TO OUTSIDE FACE OF FRAME.

COLORBOND GUTTERS & DOWNPIPES
TO COMPLY WITH PART 3.5.3 OF BCA.

ROOF PLAN
SCALE 1:100

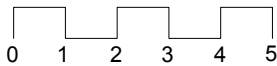

E:\w\KFEN\KLOC\img\001.png

This is a concept/draft plan based on general set-backs. Plan is subject to approval of Private Certifier / Council by-laws and rules. It may require alternation to meet the guidelines.
Plan is copyright of Fenix Homes Pty Ltd. Any use of plan without the written consent of Fenix Homes Pty Ltd may result in penalties.

SITE ADDRESS LOT NO 1422, WHITEWOOD AVENUE
CLIENT NAME MONIKA MODI & KOMAL CHOUDHARY
CONTACT NO
EMAIL ADDRESS

LOT LENGTH 32.00 METER
LOT WIDTH 12.50 METER
HOUSE LENGTH 23.65 METER
HOUSE WIDTH 11.25 METER

FRONT SET BACK PORCH: 3.26 METER
FRONT SET BACK GARAGE: 5.35 METER
SIDE SET BACK GARAGE SIDE: 1.05 METER
SIDE SET BACK OTHER SIDE: 1.05 METER
REAR SET BACK 5.09 METER

PLAN NO V2
VERSION 1
DATE 24/06/25