


NOTE BY FENIX HOMES : KINDLY FOLLOW BLUE MARKED CORRCTION IN SHEET

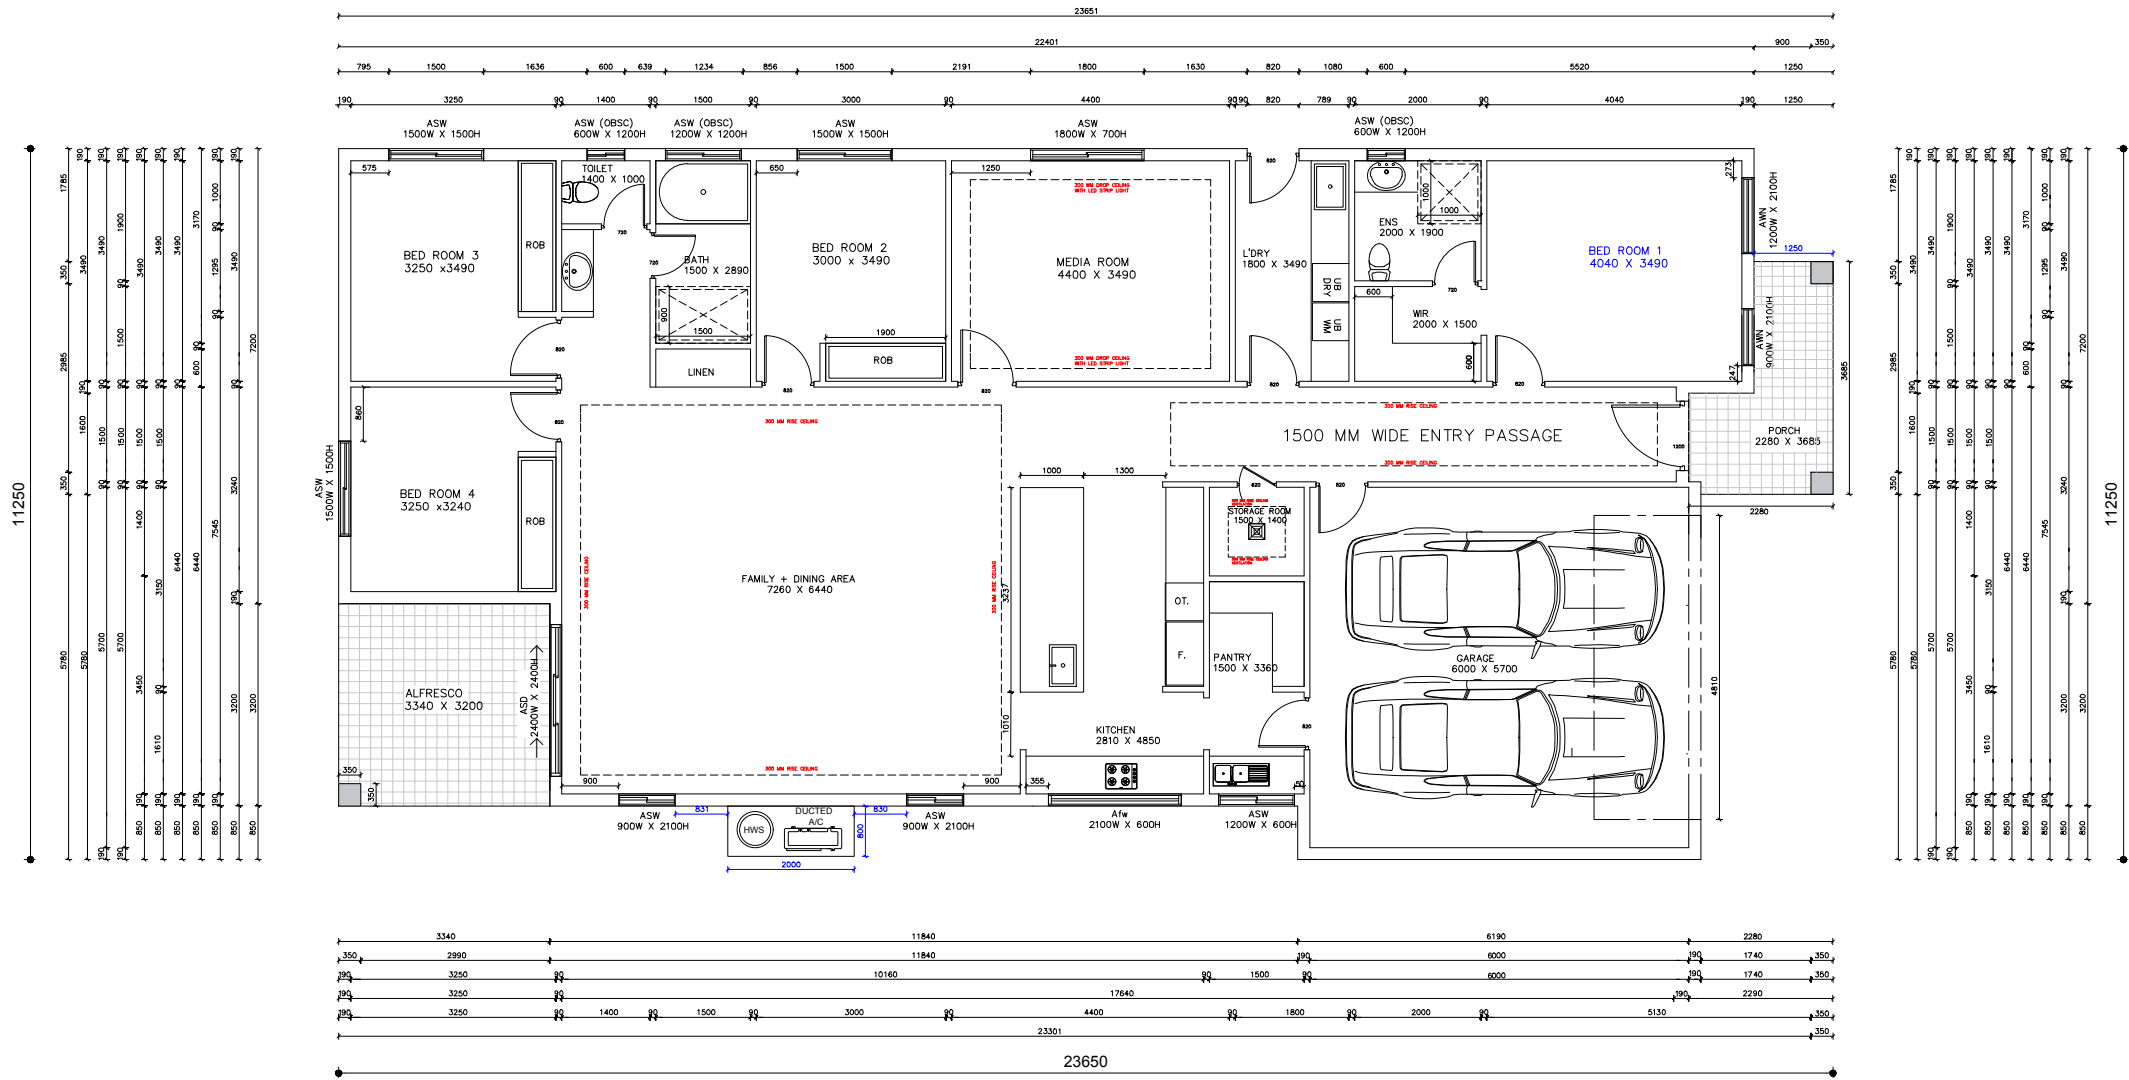

NOTES:

TRADESMAN MUST CHECK ALL DIMENSIONS & RELEVANT LEVELS ON SITE PRIOR TO SETTING OUT AND COMMENCING ANY WORK.

ALL INTERNAL DOORS TO BE 2340H U.N.O.

ALL FULL HEIGHT WINDOWS TO HAVE NO TIMBER REVEAL TO SILL.

WATER CLOSET DOORS TO BE REMOVABLE WHEN IN ACCORDANCE WITH PART 3.8.3.

DIMENSIONS NOTED ARE FRAME TO FRAME ONLY AND DO NOT TAKE PLASTERBOARD/ SKIRTING INTO CONSIDERATION.


ALL WINDOWS TO BE IN BRICK SIZES EXCLUDING ALL BAY WINDOW CONFIGURATIONS AND UNLESS OTHERWISE NOTED OR DIMENSIONED.

FOR 1st FIX CARPENTERS: ALL DOORS POSITIONED TO ALLOW FOR FULL ARCHITRAVE SURROUND UNLESS OTHERWISE NOTED.

GLASS BALUSTRADE TO COMPLY WITH AS1288 (BALCONY/VOID GLASS BARRIER TO BE PROVIDED WITH HANDRAIL INDEPENDENTLY FIXED OF THE GLASS, WHERE FALL IS MORE THAN 1M).

GROUND FLOOR PLAN

SCALE 1:100

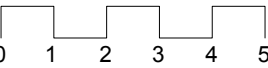

E:\work\FENIX\LOGO\image001.png	SITE ADDRESS	LOT NO 1422, WHITEWOOD AVENUE	LOT LENGTH 32.00 METER LOT WIDTH 12.50 METER HOUSE LENGTH 23.65 METER HOUSE WIDTH 11.25 METER	FRONT SET BACK PORCH: 3.26 METER FRONT SET BACK GARAGE: 5.35 METER SIDE SET BACK GARAGE SIDE: 1.05 METER SIDE SET BACK OTHER SIDE: 1.05 METER REAR SET BACK 5.09 METER	PLAN NO V2 VERSION 1 DATE 24/06/25
	CLIENT NAME	MONIKA MODI & KOMAL CHOUDHARY			
	CONTACT NO				
	EMAIL ADDRESS				

This is a concept/draft plan based on general set-backs. Plan is subject to approval of Private Certifier / Council by-laws and rules. It may require alteration to meet the guidelines. Plan is copyright of Fenix Homes Pty Ltd. Any use of plan without the written consent of Fenix Homes Pty Ltd may result in penalties.