



NOTE BY FENIX HOMES : KINDLY FOLLOW BLUE MARKED CORRCTION IN SHEET

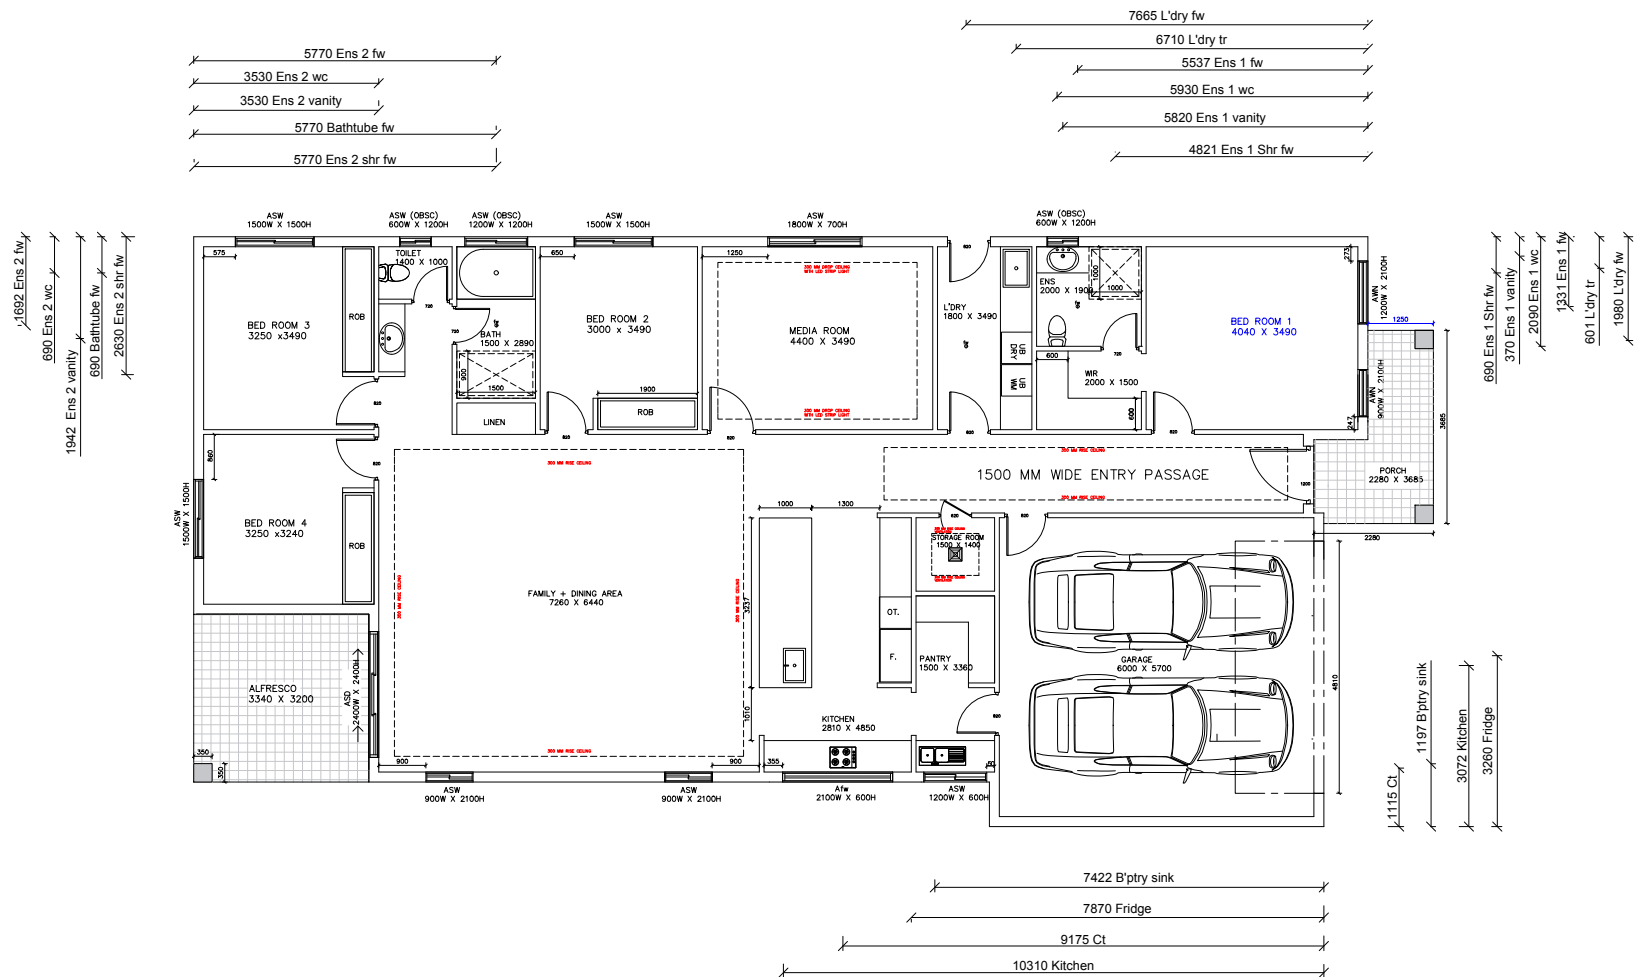

PLUMBING LAYOUT
SCALE 1:100

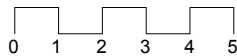

NOTES:

THE SLAB TO BE AS REQUIRED BY THE ENGINEERS AND SHALL READ FROM THEIR DRAWINGS AS WELL AS THE LAYOUT.

THE PLUMBER TO ENSURE THEY LOCATE THE SUBFLOOR PLUMBING IN RELATION TO THE FINISHED REQUIRED LOCATION. CONFIRMATION WITH THE PLUMBER TO THE SELECTED FITTINGS TO BE THE PLUMBERS RESPONSIBILITY.

0.2 POLYTHENE MEMBRANE LAPPED 200mm MIN. AND SEALED AT ALL JOINTS AND PENETRATIONS WITH AN APPROVED TAPE. 50mm MIN SAND BED.

INSTALL A PHYSICAL TERMITE BARRIER TO ALL NEW WORK. TO BE INSTALLED IN ACCORDANCE WITH AS: 3660.

	<u>SITE ADDRESS</u>	LOT NO 1422,WHITEWOOD AVENUE			<u>FRONT SET BACK PORCH:</u> 3.26 METER <u>FRONT SET BACK GARAGE:</u> 5.35 METER <u>SIDE SET BACK GARAGE SIDE:</u> 1.05 METER <u>SIDE SET BACK OTHER SIDE:</u> 1.05 METER <u>REAR SET BACK</u> 5.09 METER	<u>PLAN NO</u> V2 <u>VERSION</u> 1 <u>DATE</u> 24/06/25
	<u>CLIENT NAME</u>	MONIKA MODI & KOMAL CHOUDHARY				
	<u>CONTACT NO</u>					
	<u>EMAIL ADDRESS</u>					
		<u>LOT LENGTH</u>	32.00METER			
		<u>LOT WIDTH</u>	12.50 METER			
		<u>HOUSE LENGTH</u>	23.65METER			
		<u>HOUSE WIDTH</u>	11.25 METER			

This is a concept/draft plan based on general set-backs, Plan is subject to approval of Private Certifier / Council by-laws and rules. It may require alteration to meet the guidelines.

This is copyright of Fenix Homes Pty Ltd. Any use of Plan without the written consent of Fenix Homes Pty Ltd may result in penalty under the relevant guidelines.

This is a concept/draft plan based on general set-backs. Plan is subject to approval of Private Certifier / Council by-laws and rules. It may require alteration to meet the guidelines. Plan is copyright of Fenix Homes Pty Ltd. Any use of plan without the written consent of Fenix Homes Pty Ltd may result in penalties.