

NOTE BY FENIX HOMES : KINDLY FOLLOW BLUE MARKED CORRCTION IN SHEET

**TITLE BOUNDARIES ARE APPROXIMATE ONLY & WILL
NEED TO BE DETERMINED BY A CERTIFIED FIELD
SURVEY CARRIED OUT BY A LICENSED SURVEYOR.**

UNDERGROUND SERVICES HAVE NOT BEEN LOCATED. PRIOR TO ANY DEMOLITION, EXCAVATION OR CONSTRUCTION ON THE SITE, THE RELEVANT AUTHORITY SHOULD BE CONTACTED FOR POSSIBLE LOCATIONS OF UNDERGROUND SERVICES

BUILDER TO CHECK AND CONFIRM ALL LEVELS AND DIMENSIONS PRIOR TO COMMENCEMENT OF CONSTRUCTION

ANY DISCREPANCIES IN DOCUMENTATION AND/OR ON SITE ARE TO BE REPORTED TO THE DESIGNER BEFORE ANY WORK IS COMMENCED

**ALL WRITTEN DIMENSIONS TO TAKE PREFERENCE OVER
SCALED DIMENSIONS**

**ALL WORK TO BE IN ACCORDANCE WITH THE BUILDING
CODE OF AUSTRALIA AND RELEVANT LOCAL AUTHORITY
REQUIREMENTS**

**FOUNDATIONS, EXCAVATIONS, REINFORCEMENT PLACEMENT
ETC, TO BE INSPECTED AND APPROVED BY ENGINEER OR
BUILDING SURVEYOR PRIOR TO ANY CONCRETE PLACEMENT**

GROUND LEVELS AND FINISHED FLOOR LEVELS IF INDICATED
ARE APPROXIMATE ONLY AND ARE TO BE CONFIRMED ON SITE

NO VARIATION MAY BE MADE TO THIS DRAWING WITHOUT PRIOR
APPROVAL OF THE PROPRIETOR OR DESIGNERS

REFER TO ENGINEERS DESIGN, DOCUMENTATION, CALCULATION
AND SPECIFICATION FOR STRUCTURAL, ELECTRICAL, HYDRAULIC
AND CIVIL DETAILS (IF APPLICABLE)

**STORM WATER TO BE DISCHARGED TO STREET WATER TABLE
OR RAINWATER TANK IN ACCORDANCE WITH COUNCIL
REQUIREMENTS AND/OR DIRECTION**

**SEDIMENTS AND EROSION BARRIERS TO BE
INSTALLED AS PER LOCAL AUTHORITY REQUIREMENTS**

SURFACE WATER RUN-OFF FROM NOT LESS THAN 50M² OF ROOF CATCHMENT AREA TO BE STORED IN A RAINWATER TANK AND, PLUMBED TO EITHER A TOILET, WATER HEATER OR LAUNDRY COLD WATER AND, INLET/OVERFLOW ON RAIN WATER TANK MUST BE FITTED WITH INSECT PROOF AND NON-DEGRADABLE SCREENS

**MINI. SIZE 1000 LITRES TANK FOR STORMWATER
DETENTION. REFER TO ENG'S SITEWORK &
DRAINAGE PLANS**

RAINWATER TANK:

-CONNECTED TO

-AT LEAST 60% ROOF AREA
-A TOILET & THE LAUNDRY COLD WATER OUTLETS

-INCLUDES A 20-25MM DIAMETER SLOW RELEASE ORIFACE AT BOTTOM OF THE DETENTION COMPONENT OF TANK

3000L RAINWATER TANK

-2000L RETENTION
-1000L DETENTION

BOUNDARY FENCING :


SIDE AND REAR BOUNDARY FENCES MUST BE A MAXIMUM 1.8M IN HEIGHT AND MUST BE CONSTRUCTED FROM 'GOOD NEIGHBOUR' CUSTOM ORB PROFILE IN TIMBER® GREY RIDGE® OR WOODLAND GREY®."

FENCING DOOR :

**RETURN FENCE AND GATE MUST BE 1M BEHIND FRONT FACADE,
PAINTED DARK GREY / BLACK OR TO MATCH DWELLING**

LETTER BOX :


LATTER BOX RENDERED OR AS PER DG'S

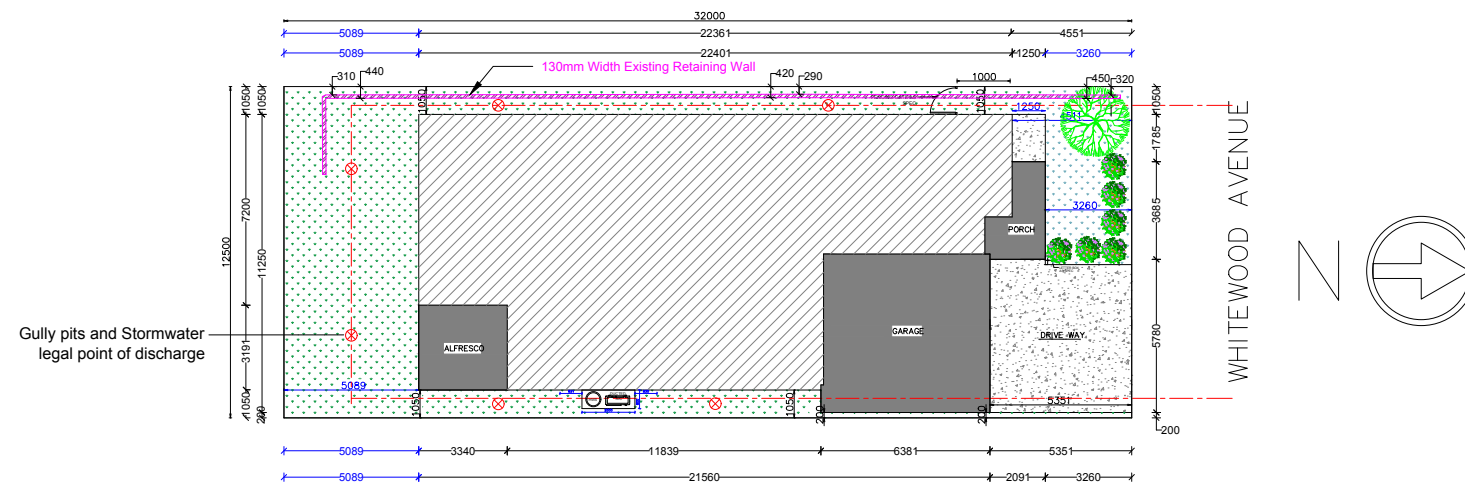


LANDSCAPE SCHEDULE				
NO.	BOTANICAL NAME	COMMON NAME	HEIGHT	SPREAD
<u>TREES:</u>				
①	Corymbia eximia 'Nana'	Yellow Bloodwood	7 to 8m	6 to 7m
②	Hoheria lyallii	Mountain Ribbonwood	4 to 6m	2 to 3m
③	Carpinus betulus	Fastigiata	5 to 8m	1 to 2m
<u>SHRUBS:</u>				
④	Acacia suaveolens	Sweet-scented Wattle	0.3 to 1.5m	0.3 to 1.5m
⑤	Acacia cognata	Bower Beauty	1.0 to 1.0m	1.0 to 1.0m
<u>GROUND COVER:</u>				
⑥	Babingtonia virgata	Nana	0.3 to 0.5m	0.5 to 1.0m
⑦	Crowea	Festival	1.0 to 1.5m	1.0 to 1.5m
⑧	Ajuga reptans	Catlin's Giant	0.1 to 0.2m	0.3 to 0.5m
⑨	Astroloma humifusum	Native Cranberry	0.1 to 0.5m	0.5 to 1.5m

SITE PLAN

SCALE 1:200

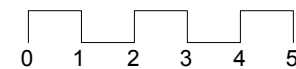

 	<u>SITE ADDRESS</u>	LOT NO 1422,WHITEWOOD AVENUE						
	<u>CLIENT NAME</u>	MONIKA MODI & KOMAL CHOUDHARY	<u>LOT LENGTH</u>	32.00 METER	<u>FRONT SET BACK PORCH:</u>	3.26 METER	<u>PLAN NO</u>	V2
	<u>CONTACT NO</u>		<u>LOT WIDTH</u>	12.50 METER	<u>FRONT SET BACK GARAGE:</u>	5.35 METER	<u>VERSION</u>	1
	<u>EMAIL ADDRESS</u>		<u>HOUSE LENGTH</u>	23.65 METER	<u>SIDE SET BACK GARAGE SIDE:</u>	1.05 METER	<u>DATE</u>	24/06/25
			<u>HOUSE WIDTH</u>	11.25 METER	<u>SIDE SET BACK OTHER SIDE:</u>	1.05 METER		
			<u>REAR SET BACK</u>	5.09 METER				
This is a concept/draft plan based on general set-backs. Plan is subject to approval of Private Certifier / Council by-laws and rules. It may require alteration to meet the guidelines.								