
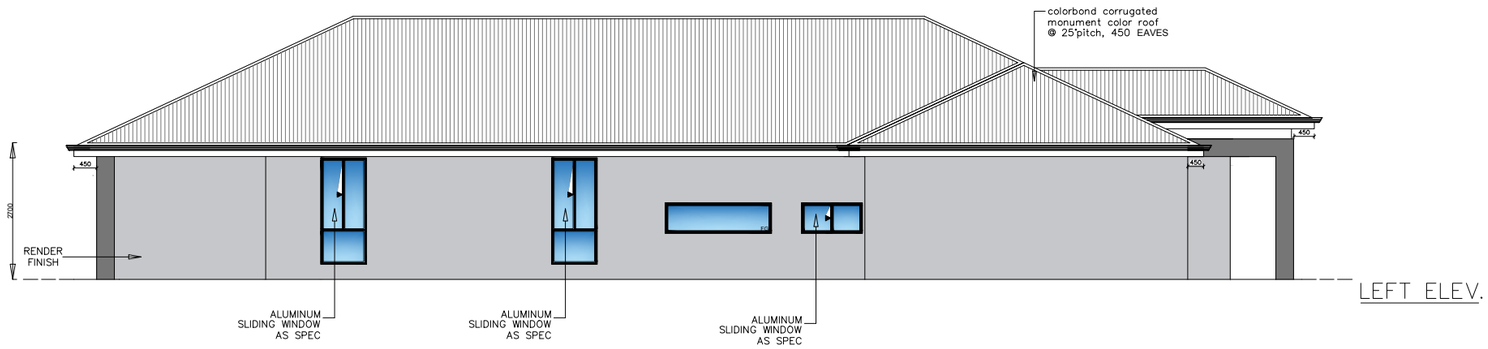


FRONT ELEVATION

SCALE 1:100

0 1 2 3 4 5

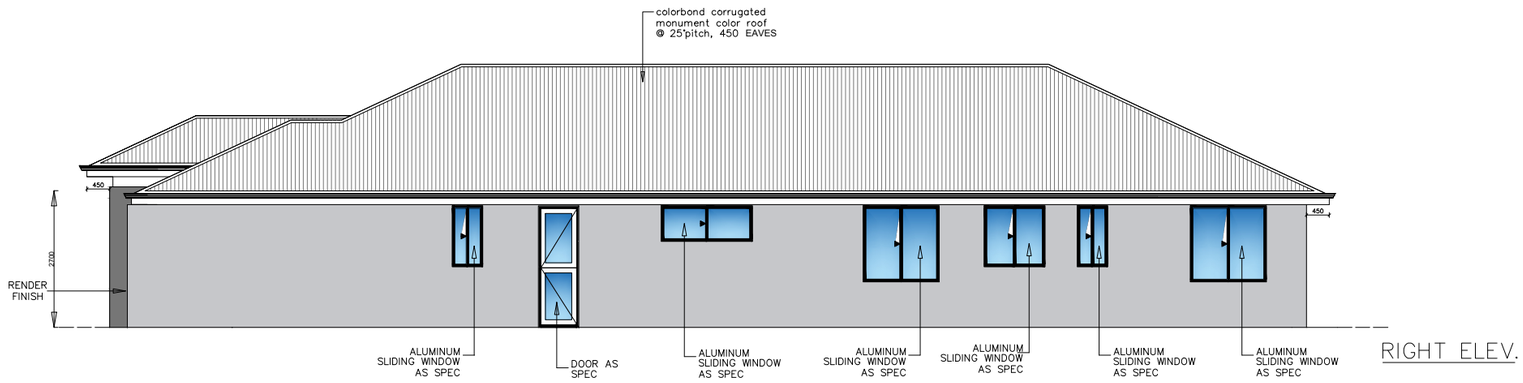

REAR ELEVATION

SCALE 1:100

0 1 2 3 4 5

NOTES:

- ALL MATERIALS TO BE INSTALLED IN ACCORDANCE WITH MANUFACTURERS SPECIFICATIONS AND INSTALLATION DETAILS.
- ONLY A TYPICAL DESCRIPTION OF FINISHES ARE SHOWN. REFER TO BUILDING SPECIFICATION FOR FURTHER INFORMATION.
- PAINT FINISH INFILL PANEL OVER ALL OPENINGS WITHIN BRICKWORK UNLESS NOTED OTHERWISE.
- ALL UPPER STOREY WINDOWS TO BE BUILT WITH FALL PROTECTION.
- CLADDING CORNERS AS PER MANUFACTURER'S SPECIFICATION.
- BALCONY TO BE WATERPROOFED AS PER A.S. 4654 PARTS 1 & 2.
- STAIRS TO COMPLY WITH PART 3.9.1 OF THE BCA BALUSTRADES/HANDRAILS TO COMPLY WITH PART 3.9.2 OF THE BCA.
- STORMWATER TO BE DISCHARGE TO LEGAL POINT AND SURFACE WATER DRAINAGE TO COMPLY WITH CLAUSE 3.1.3.3 OF THE BCA.
- OPENABLE BEDROOM WINDOWS TO COMPLY WITH PART 3.9.2.6 OF THE BCA.
- GLASS BALUSTRADE TO COMPLY WITH AS 1288–2006 PART 7.3.6.
- SMOKE ALARMS TO COMPLY WITH PART 3.7.5 OF THE BCA AND MUST BE INTERCONNECTED.
- GUTTERS & DOWNPIPES TO COMPLY WITH PART 3.5.3 OF THE BCA.
- ALL WINDOWS HEAD HEIGHTS TO BE AT 2400mm HIGH, UNLESS OTHERWISE NOTED.
- REFER TO ENGINEER'S DESIGN AND DOCUMENTATION FOR ALL CONTROL JOINT LOCATIONS.

E:\work\FENIX\LOGO\image001.png

SITE ADDRESS	LOT NO 1422,WHITEWOOD AVENUE
CLIENT NAME	MONIKA MODI & KOMAL CHOUDHARY
CONTACT NO	
EMAIL ADDRESS	

LOT LENGTH	32.00METER
LOT WIDTH	12.50 METER
HOUSE LENGTH	23.65METER
HOUSE WIDTH	11.25 METER

FRONT SET BACK PORCH:	3.26 METER
FRONT SET BACK GARAGE:	5.35 METER
SIDE SET BACK GARAGE SIDE:	1.05 METER
SIDE SET BACK OTHER SIDE:	1.05 METER
REAR SET BACK	5.09 METER

PLAN NO	V2
VERSION	1
DATE	24/06/25

This is a concept/draft plan based on general set-backs, Plan is subject to approval of Private Certifier / Council by-laws and rules. It may require alternation to meet the guidelines.
Plan is copyright of Fenix Homes Pty Ltd. Any use of plan without the written consent of Fenix Homes Pty Ltd may result in penalties.